




Daglichtberekening


Kozijnmerken, overzicht gevels



Tuingevel

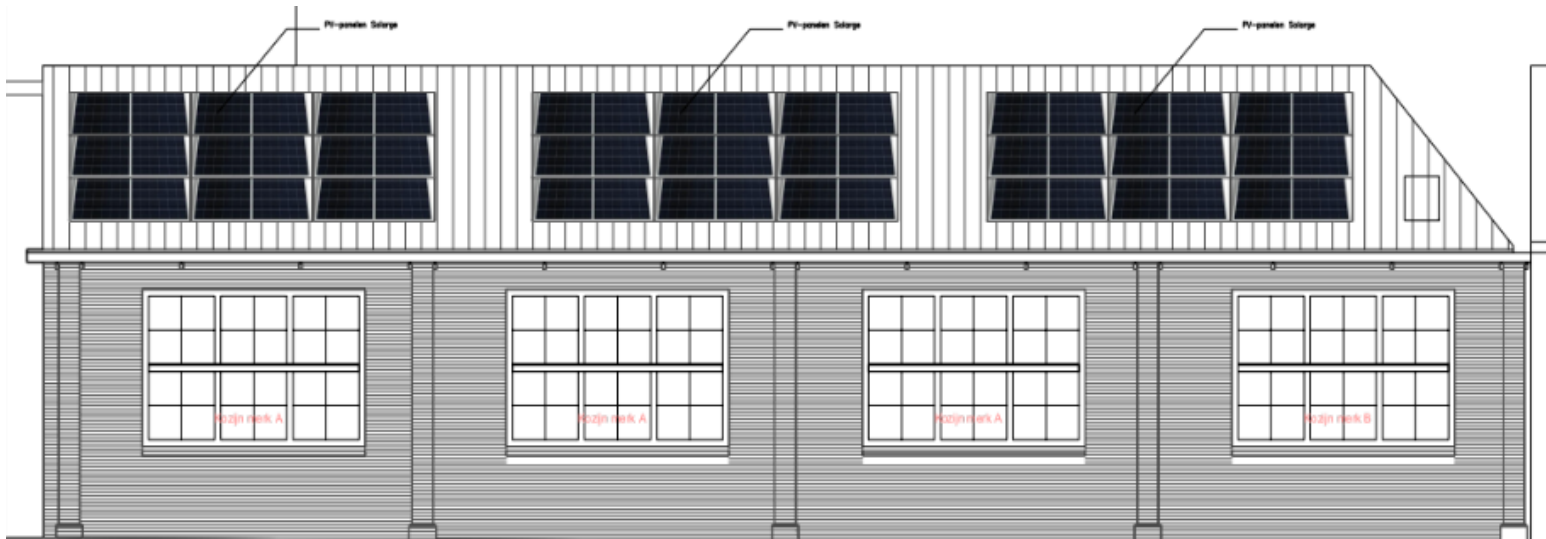


Gevel Ploenstraat

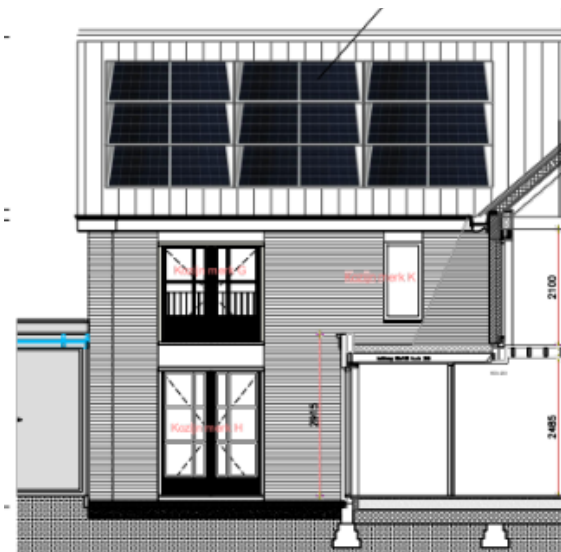

Aanzicht:
Gevel Herenstraat

← binnengevel

buitengevel →

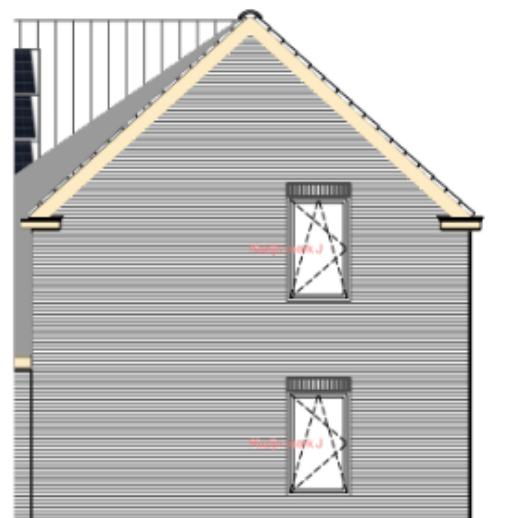

Gebruiksoppervlakken		GBO	VBO	bruto inh
ruimtenr.	bouwbesluit	m2	m2	m3
Woningtype A	3stk			
Begane grond	verblijfsruimte	60,2	45,5	
1* verdieping	verblijfsruimte	27	26,8	
totaal		87,2	72,3	343
VBO (min. 55% van GBO)=		ca.48	voldoet	
Woningtype B	1e Verdieping			
1* verdieping	verblijfsruimte	86,7	69,2	
totaal		86,7	69,2	350
VBO (min. 55% van GBO)=		ca.49	voldoet	
Woningtype B	Begane grond			
begane grond	verblijfsruimte	88	68,6	
totaal		88	68,6	270
VBO (min. 55% van GBO)=		ca.48,5	voldoet	

Daglichtberekening		
Woningtype A	3stk	
Kozijnmerk	Ae(m2)	Aantal stuks
A	8,4	1
E	6	1
F	1,44	1
Ae totaal	15,8	voldoet
Ae benodigd (min. 10% VBO)= 7,2		
Woningtype B	1e Verdieping	
Kozijnmerk	Ae(m2)	Aantal stuks
B	4,2	1
C	4	1
D	0,5	1
G	2,5	1
K	0,7	1
L	0,8	1
Ae totaal	12,7	voldoet
Ae benodigd (min. 10% VBO)= 6,92		
Woningtype B	Begane grond	
Kozijnmerk	Ae(m2)	Aantal stuks
B	4,2	1
C	3,96	1
H	2,4	1
Ae totaal	10,56	voldoet
Ae benodigd (min. 10% VBO)= 6,86		

berekening vl. NEN 2580 en NTA 2581